




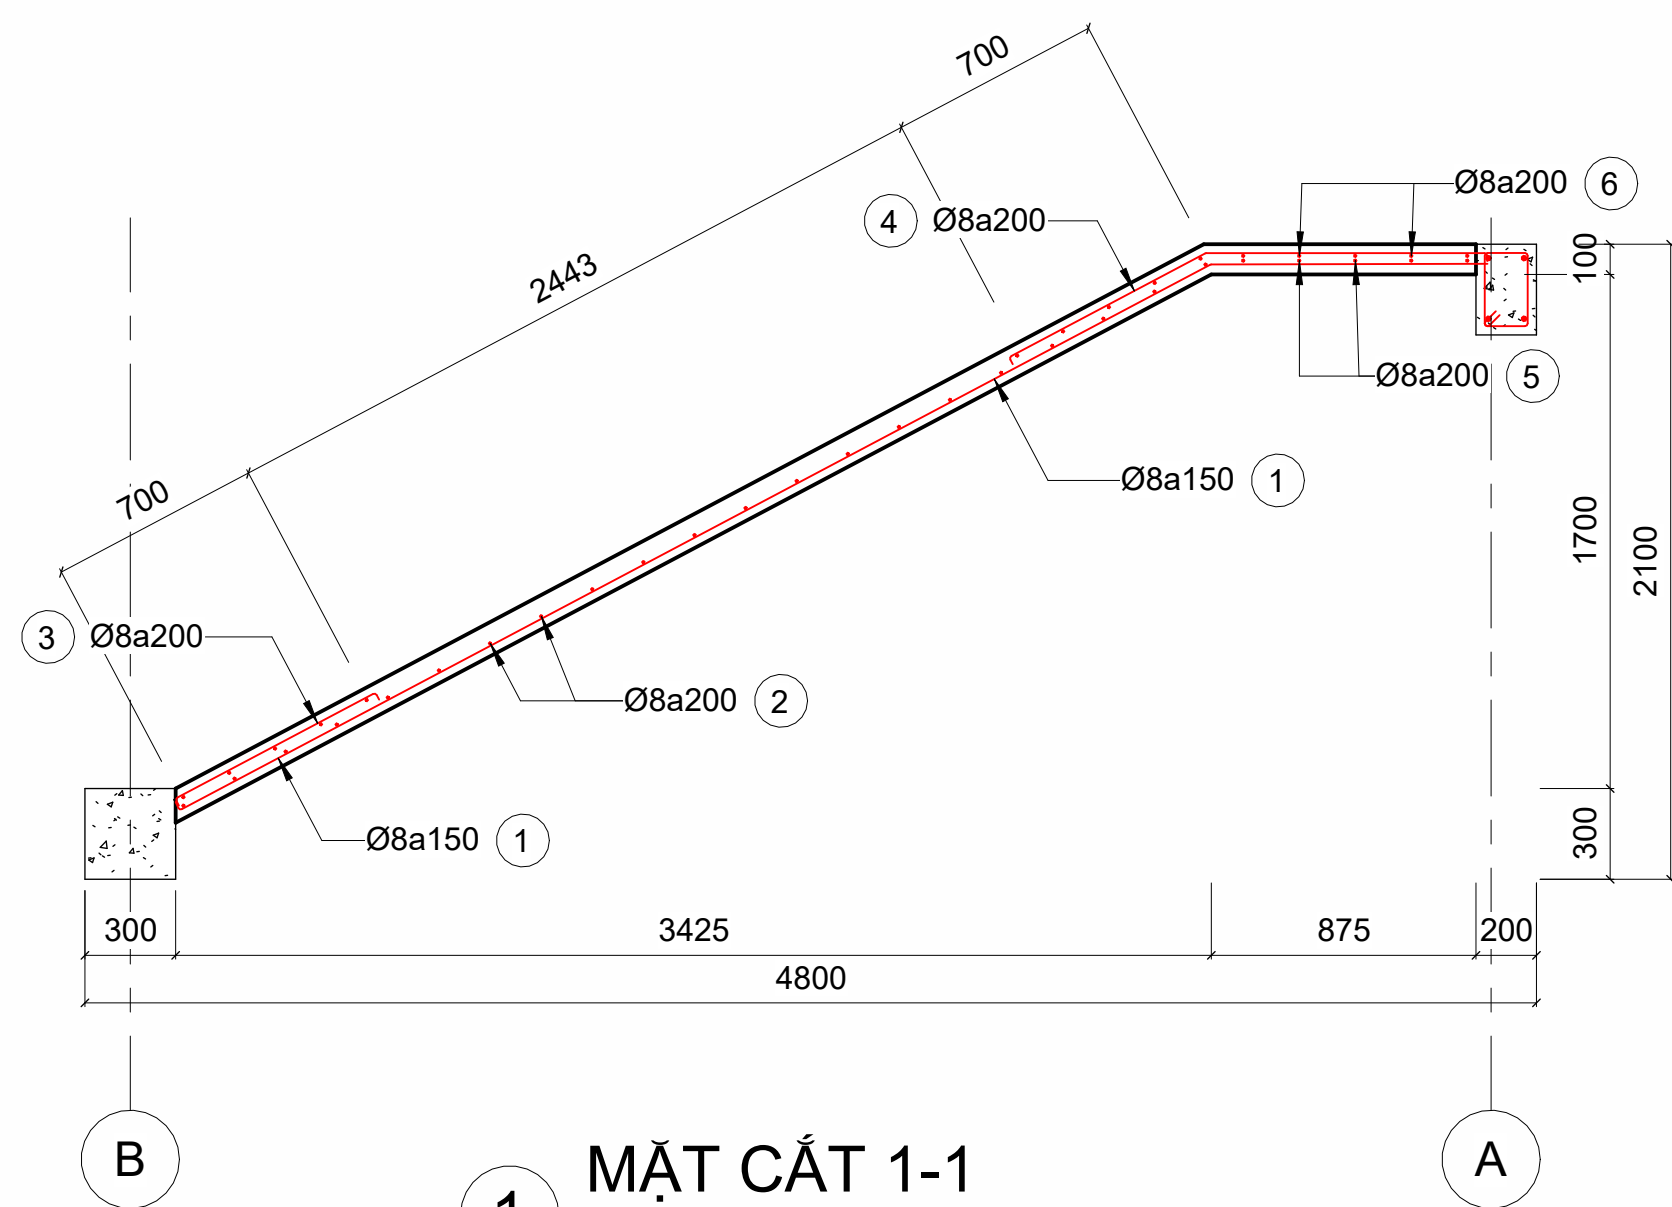


1 MẶT CẮT 1-1
1 : 25

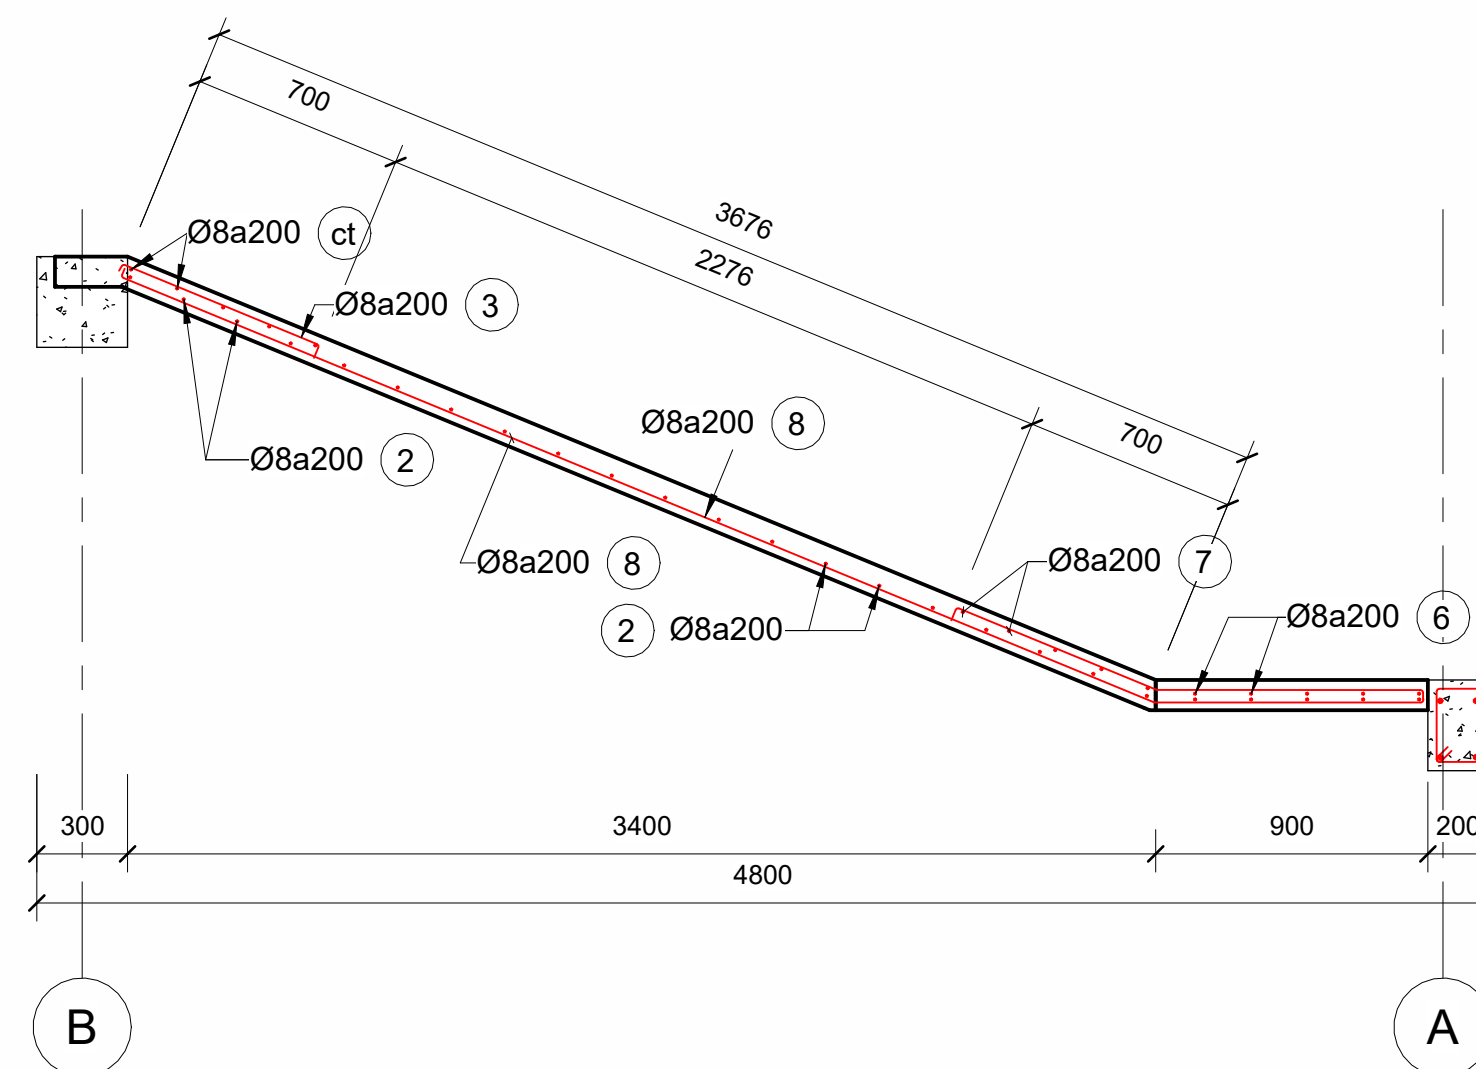


4 MẶT CẮT 3-3
1 : 25

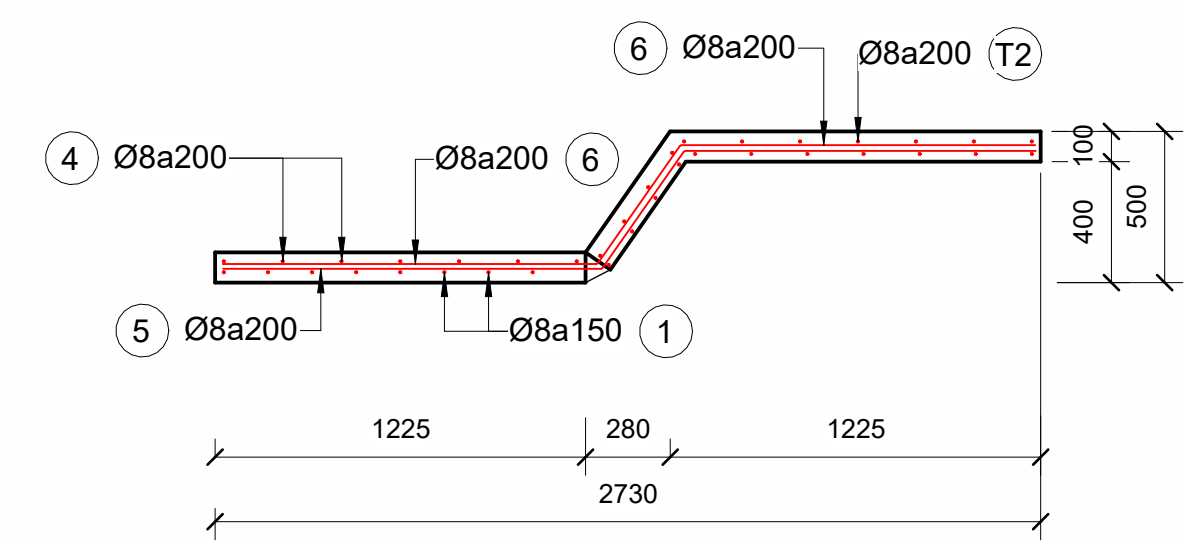


2 MẶT CẮT 2-2
1 : 25

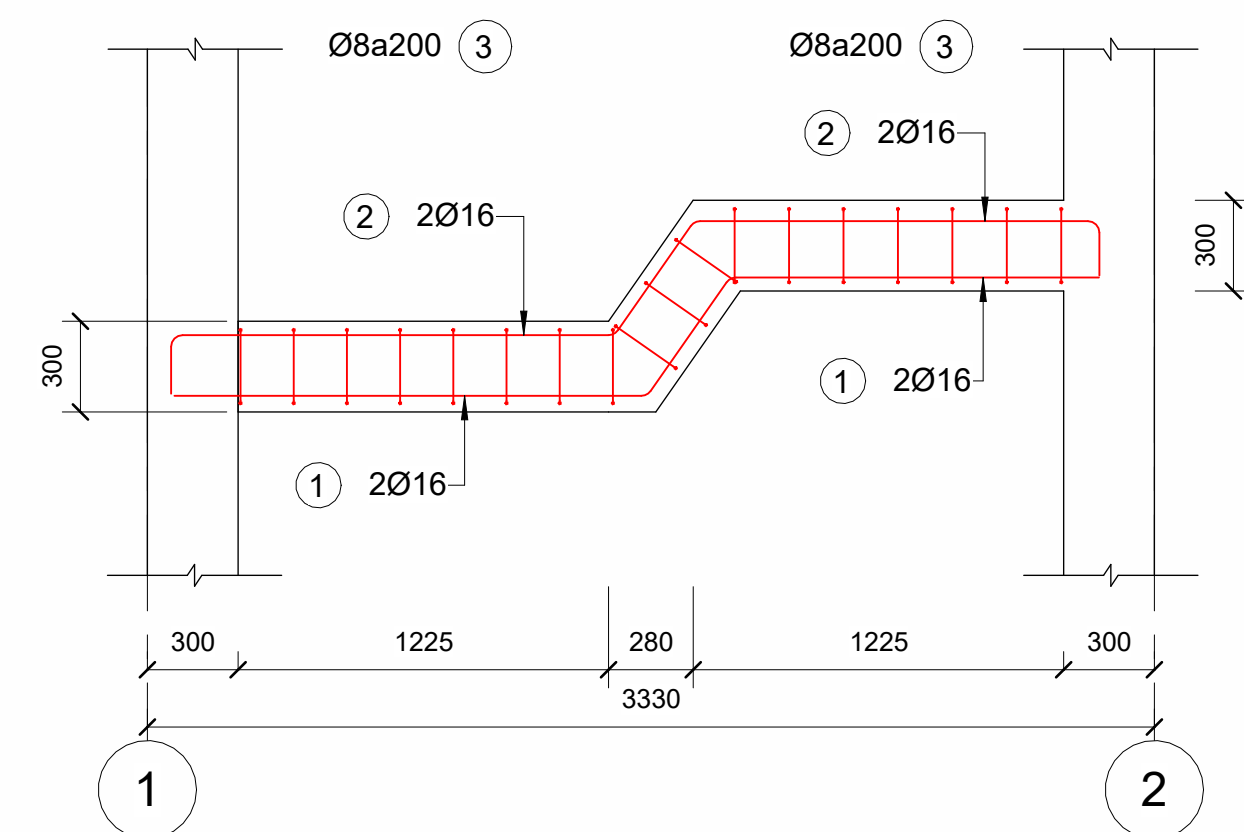


6 MẶT CẮT DẦM CHIỀU NGHỈ
1 : 25

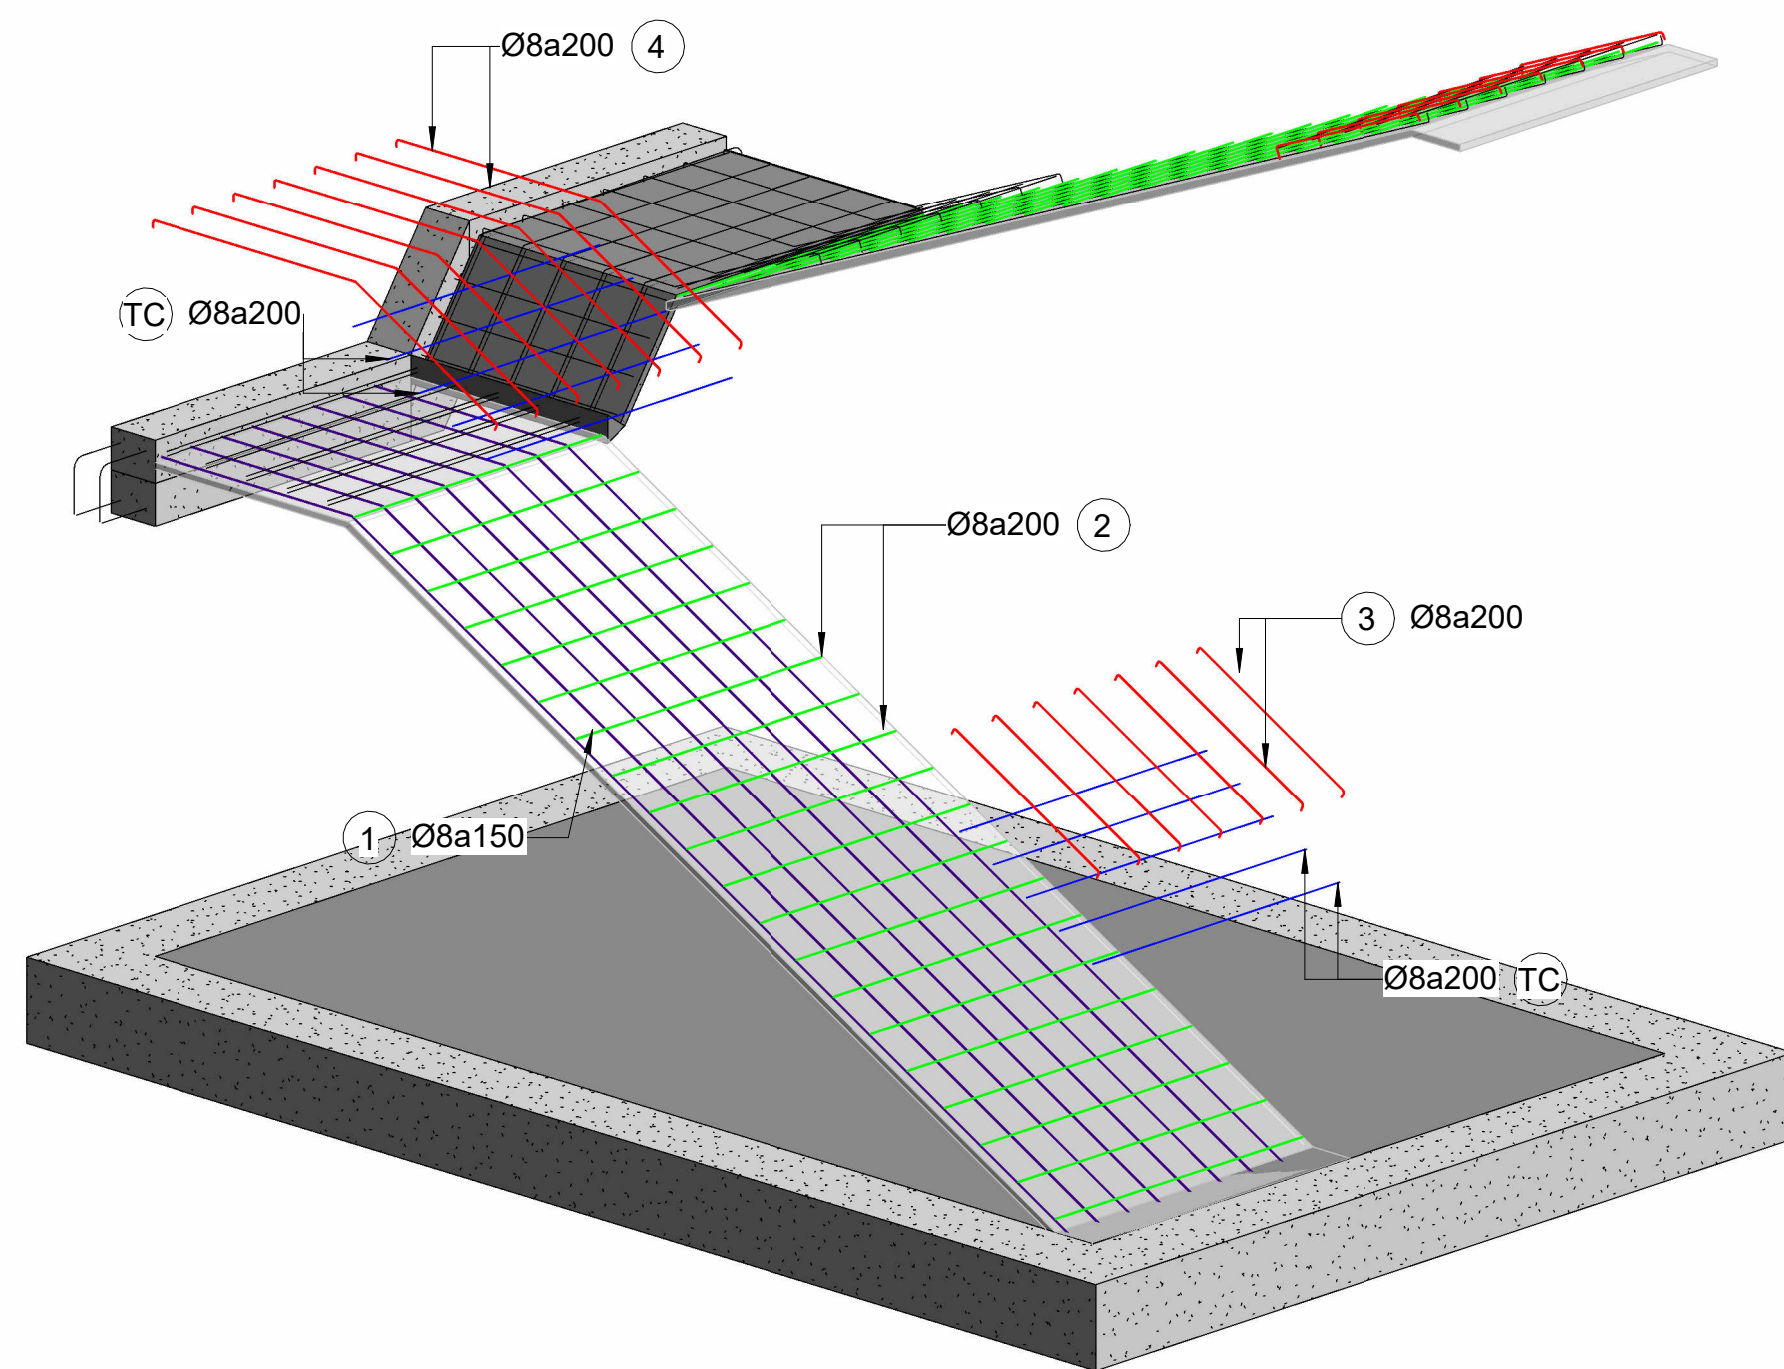

5 3D CẦU THANG BẢN 1

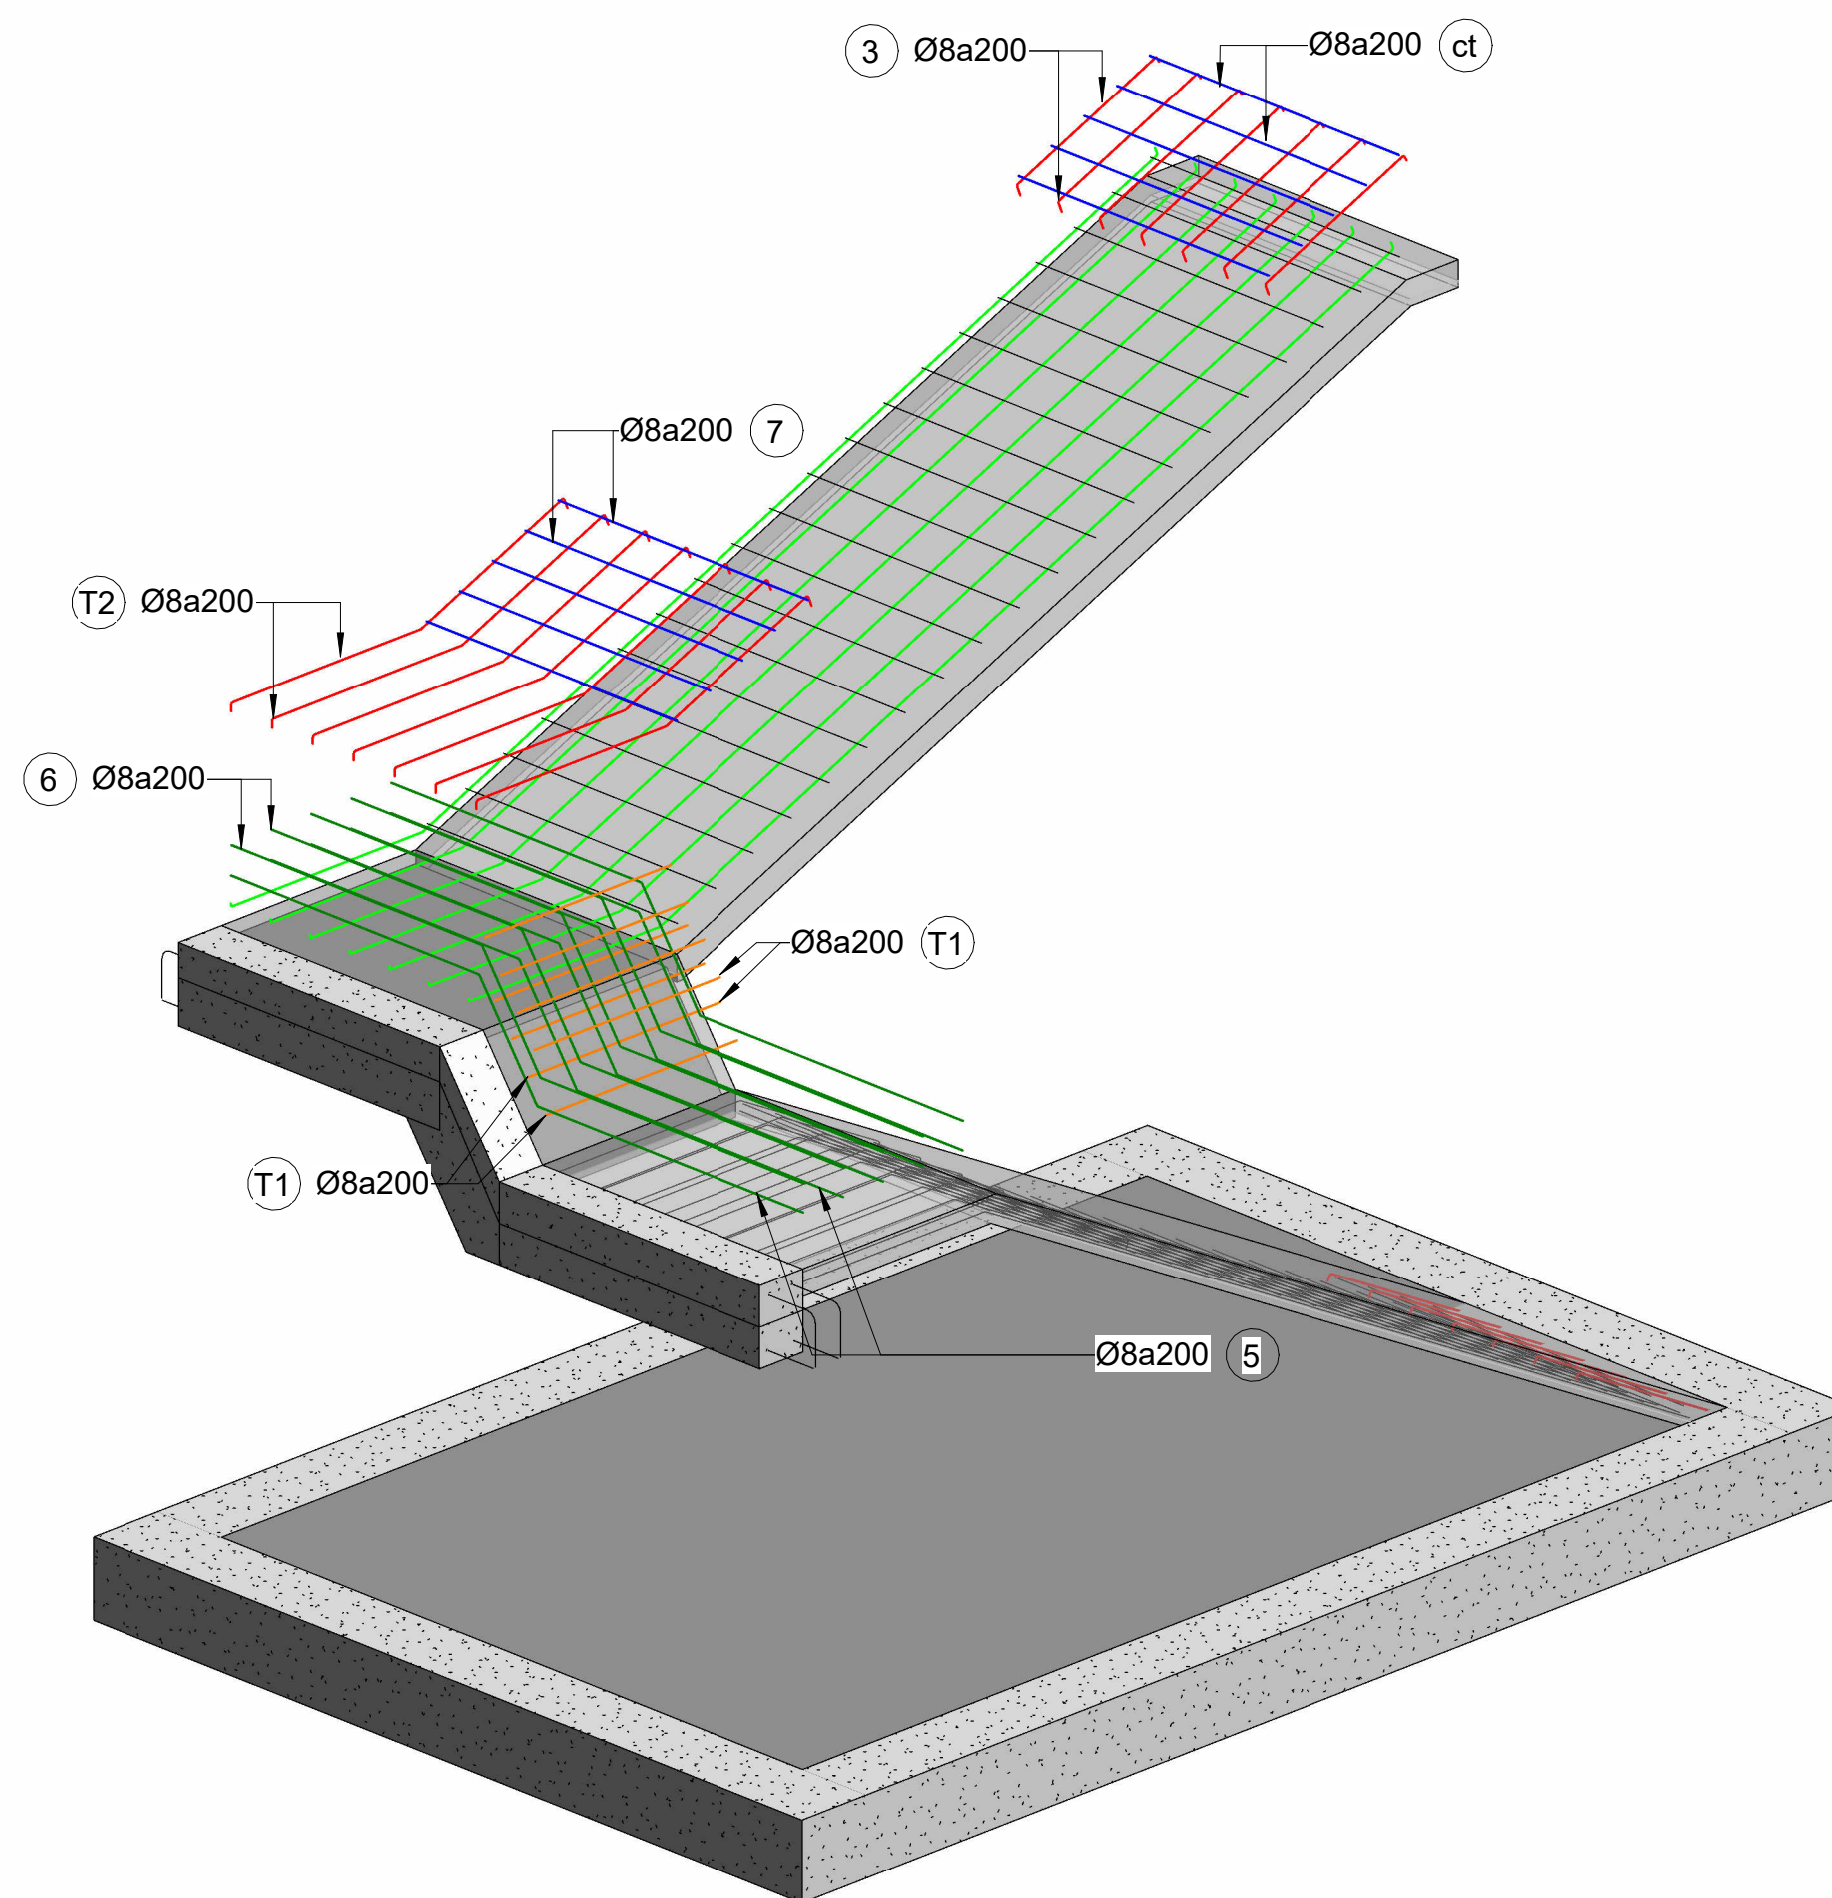

3 3D CẦU THANG BẢN 2

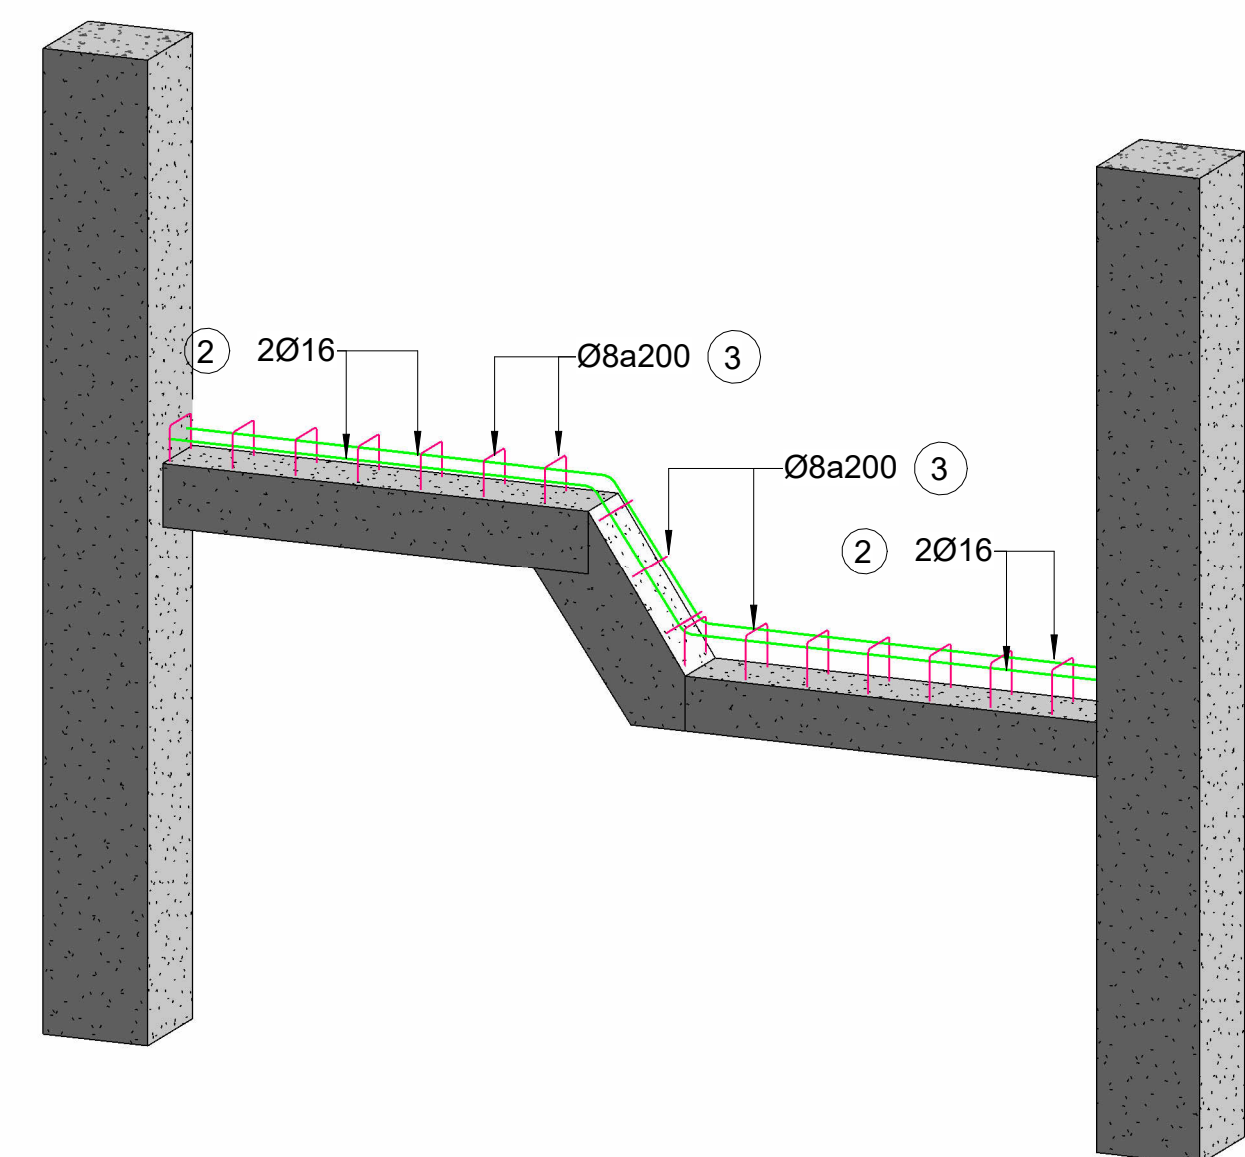

7 3D DẦM CHIỀU NGHỈ